


Guillaume Dullier

Investi - astucieux - perfectionniste

41 ans - 06 10 26 29 35

guillaumedullier@hotmail.fr

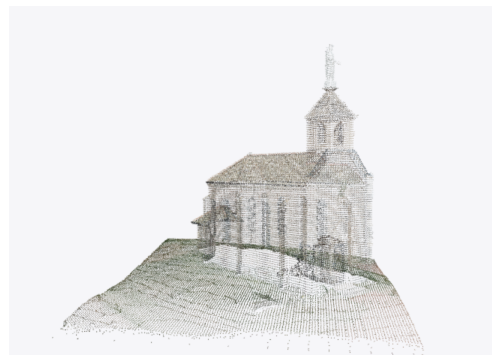

BIM Modeleur

Dessinateur projeteur en bâtiment

FORMATIONS

2025 – Titre professionnel BIM Modeleur du Bâtiment (Bac+2)

2014 – CAP Menuisier d'agencement

EXPÉRIENCES

01/2024 12/2024 : Collaboration – Edouard de Vimal, Architecte DE

06/2022 05/2023 : Charpentier – Alliance Bois Métal

05/2021 02/2022 : Agent de production – 21 Degrés Sud

03/2017 03/2020 : Menuisier cintreur – Formalis

01/2016 12/2016 : Réhabilitation – Particulier

09/2015 11/2015 : Pressage fermettes/ossature bois – COBA

03/2015 08/2015 : Menuisier – Société Santailler

09/2014 11/2014 : Stagiaire – Menuiserie Pourtaud Yohan

2013 : Technicien – Alex Cobas, designer, artiste (42)

2011 - 2012 : Interimaire – Affaires à suivre, événementiel.

2009 - 2010 : Facteur d'équipe – La Poste

2008 - 2009 : Opérateur de saisie – Police Technique et scientifique

COMPÉTENCES

Revit ****

Metashape ***

Suite Adobe ***

PostShot **

AutoCAD **

Vectorworks **

Reality Capture **

Recap **

Blender *

Langues & Permis

- Anglais – compréhension écrite avancée : Lecture au quotidien de contenus variés : documentations techniques, tutoriels, rapports open source et papiers de recherche

- Permis B





Centres d'intérêt


Photogrammétrie, Gaussian Splatting, Edge detection, Cyclisme de loisir...

mon CV en ligne,
avec mon portfolio :






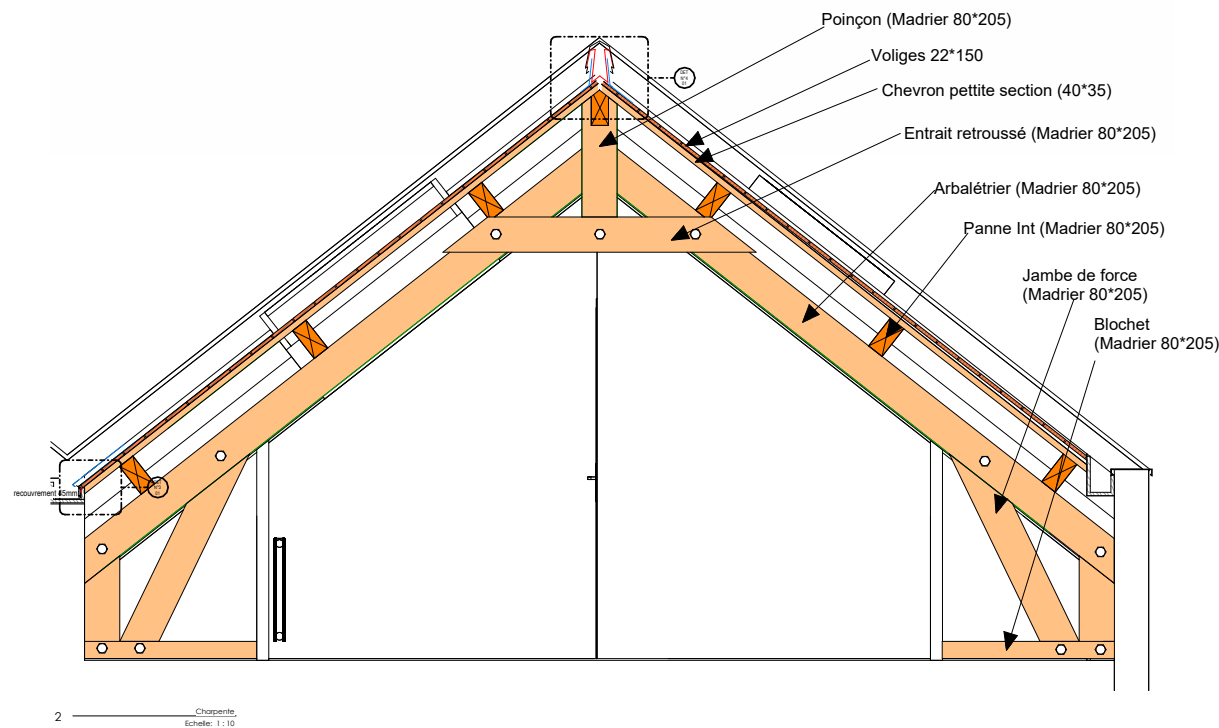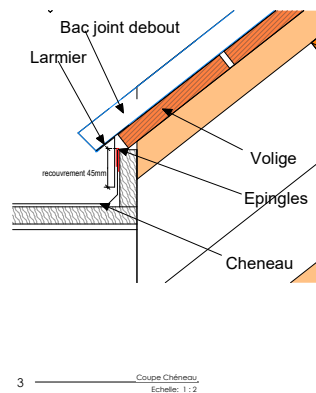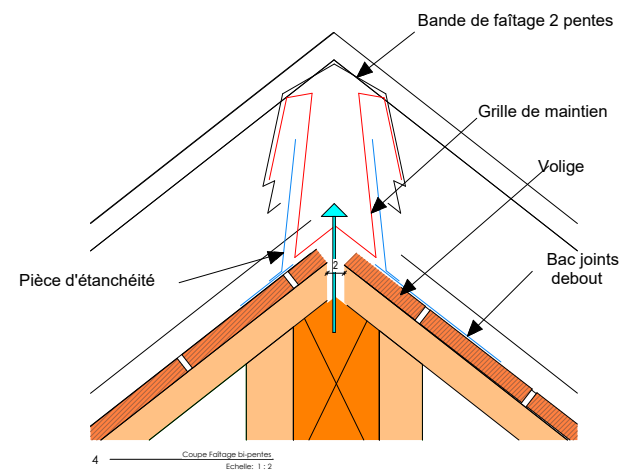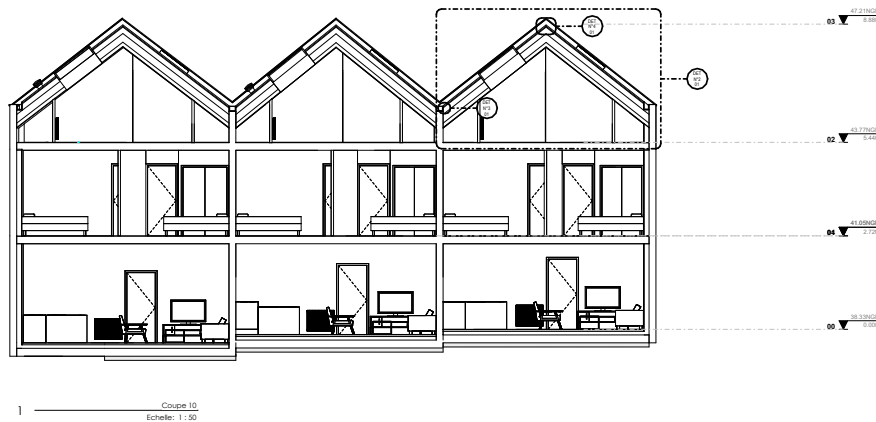

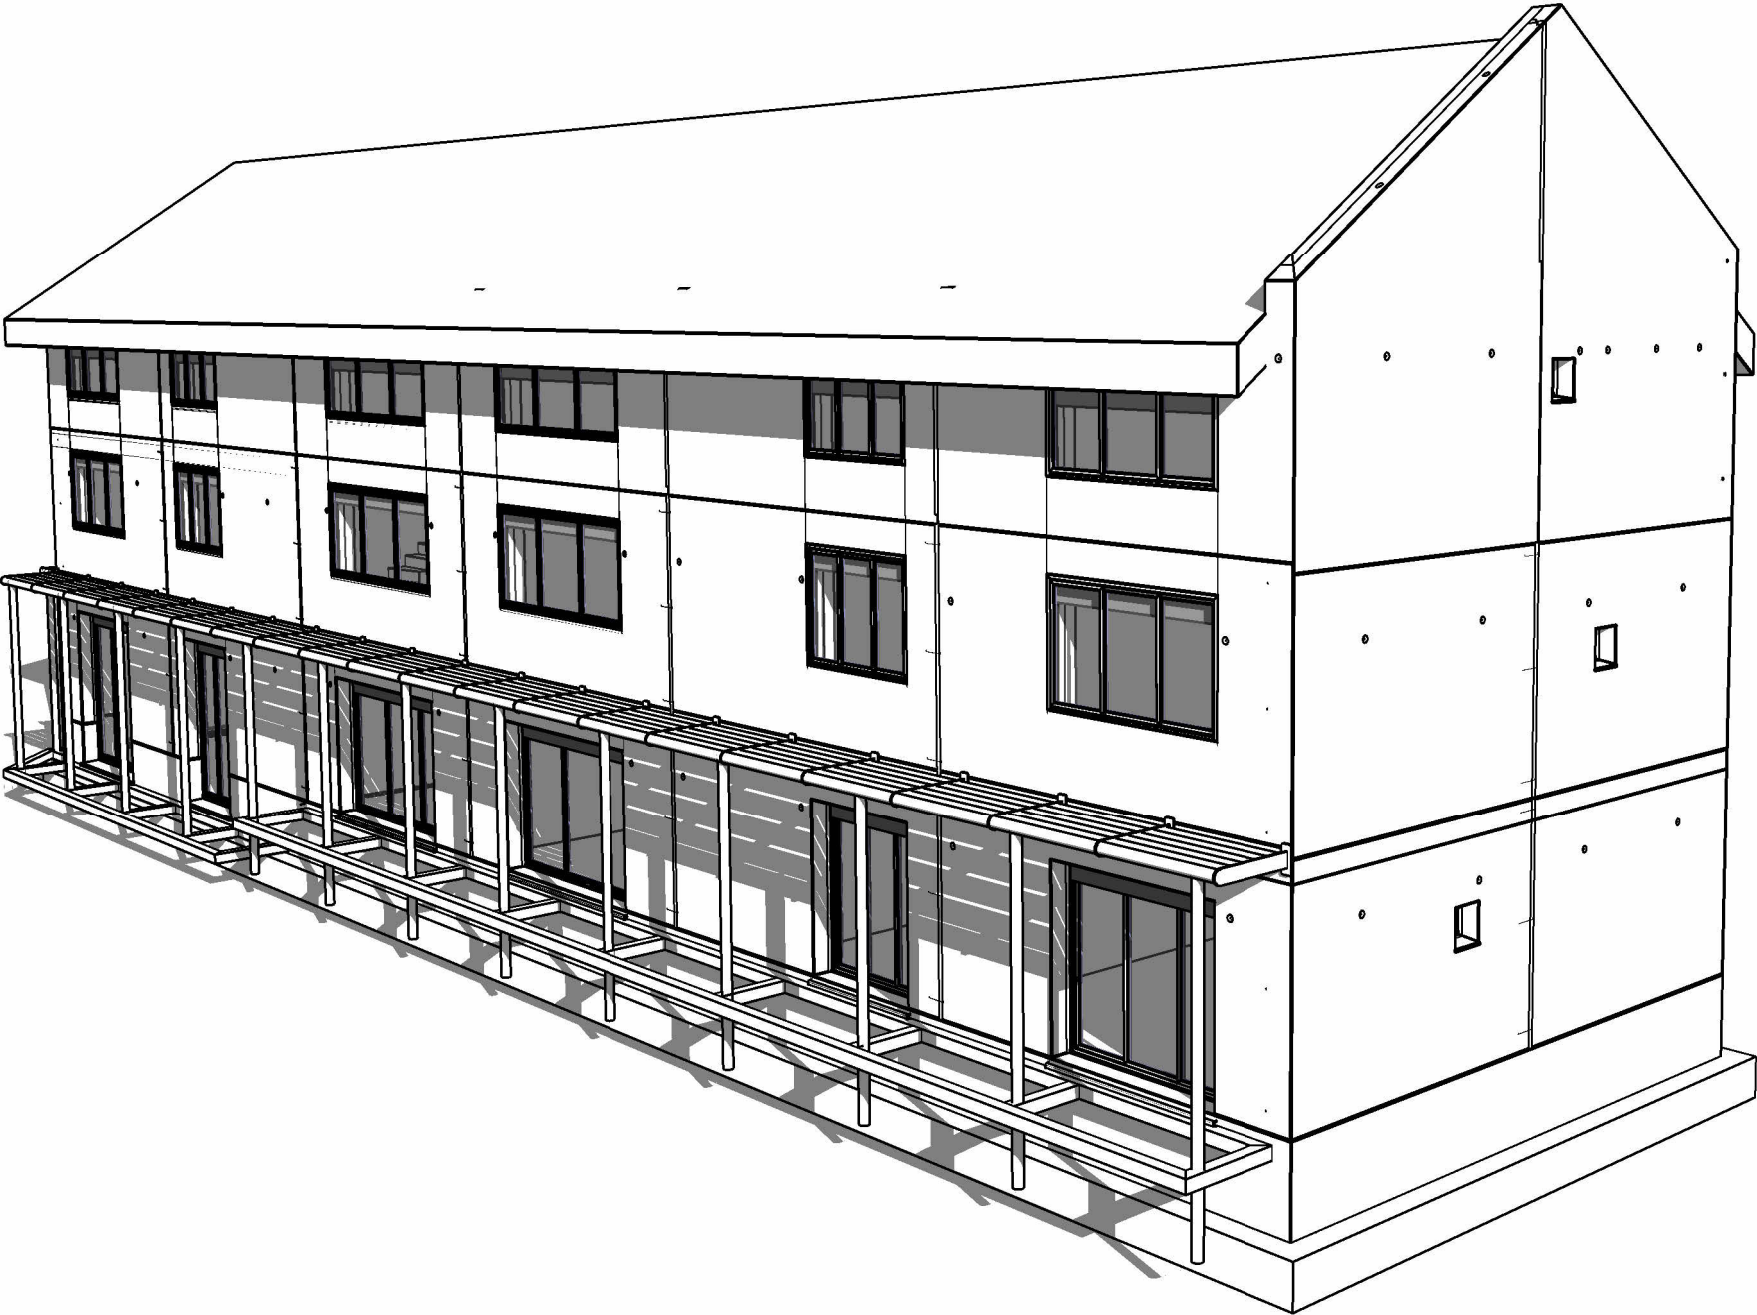

Ce document est un support pédagogique, en aucun cas il ne doit être exploité comme document réel.


Colmar	Guillaume Dullier	20/06/2024	
	Coopérative de logements		
	angle sud-est		A-100






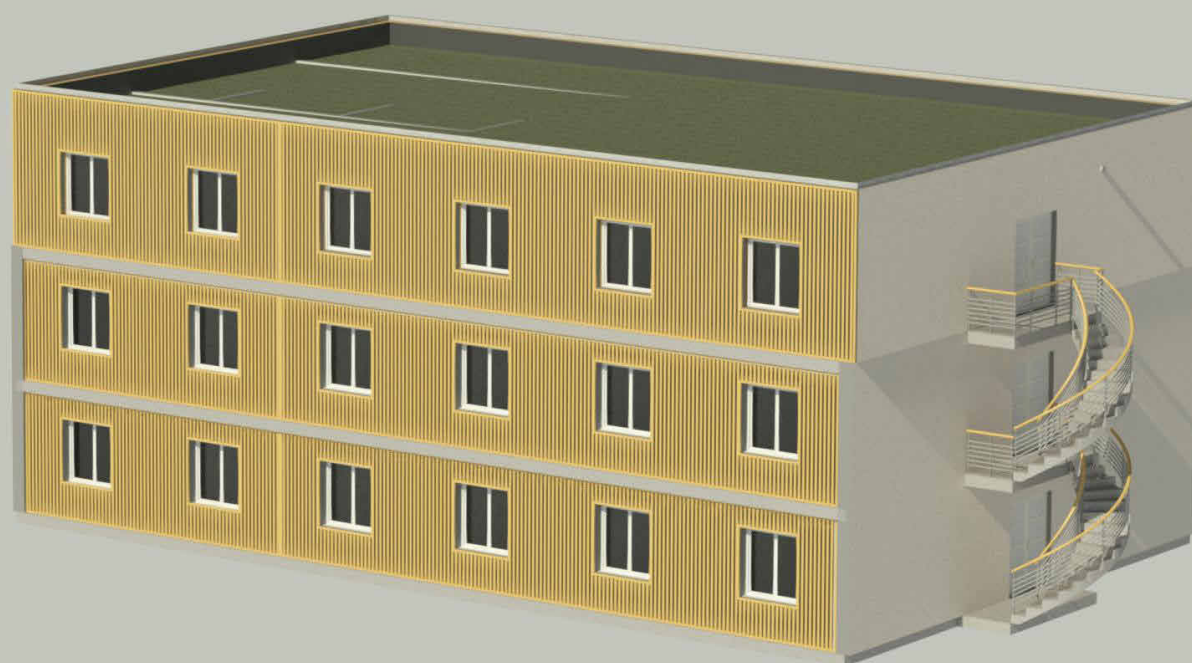



Ce document est un support pédagogique, en aucun cas il ne doit être exploité comme document réel.

Colmar	Guillaume Dullier	25/06/2024	1 : 1
	Beach Motel		
	Perspectives		A108

Salon
43 rue de la République
69220 Belleville
Dallien 08/07/24

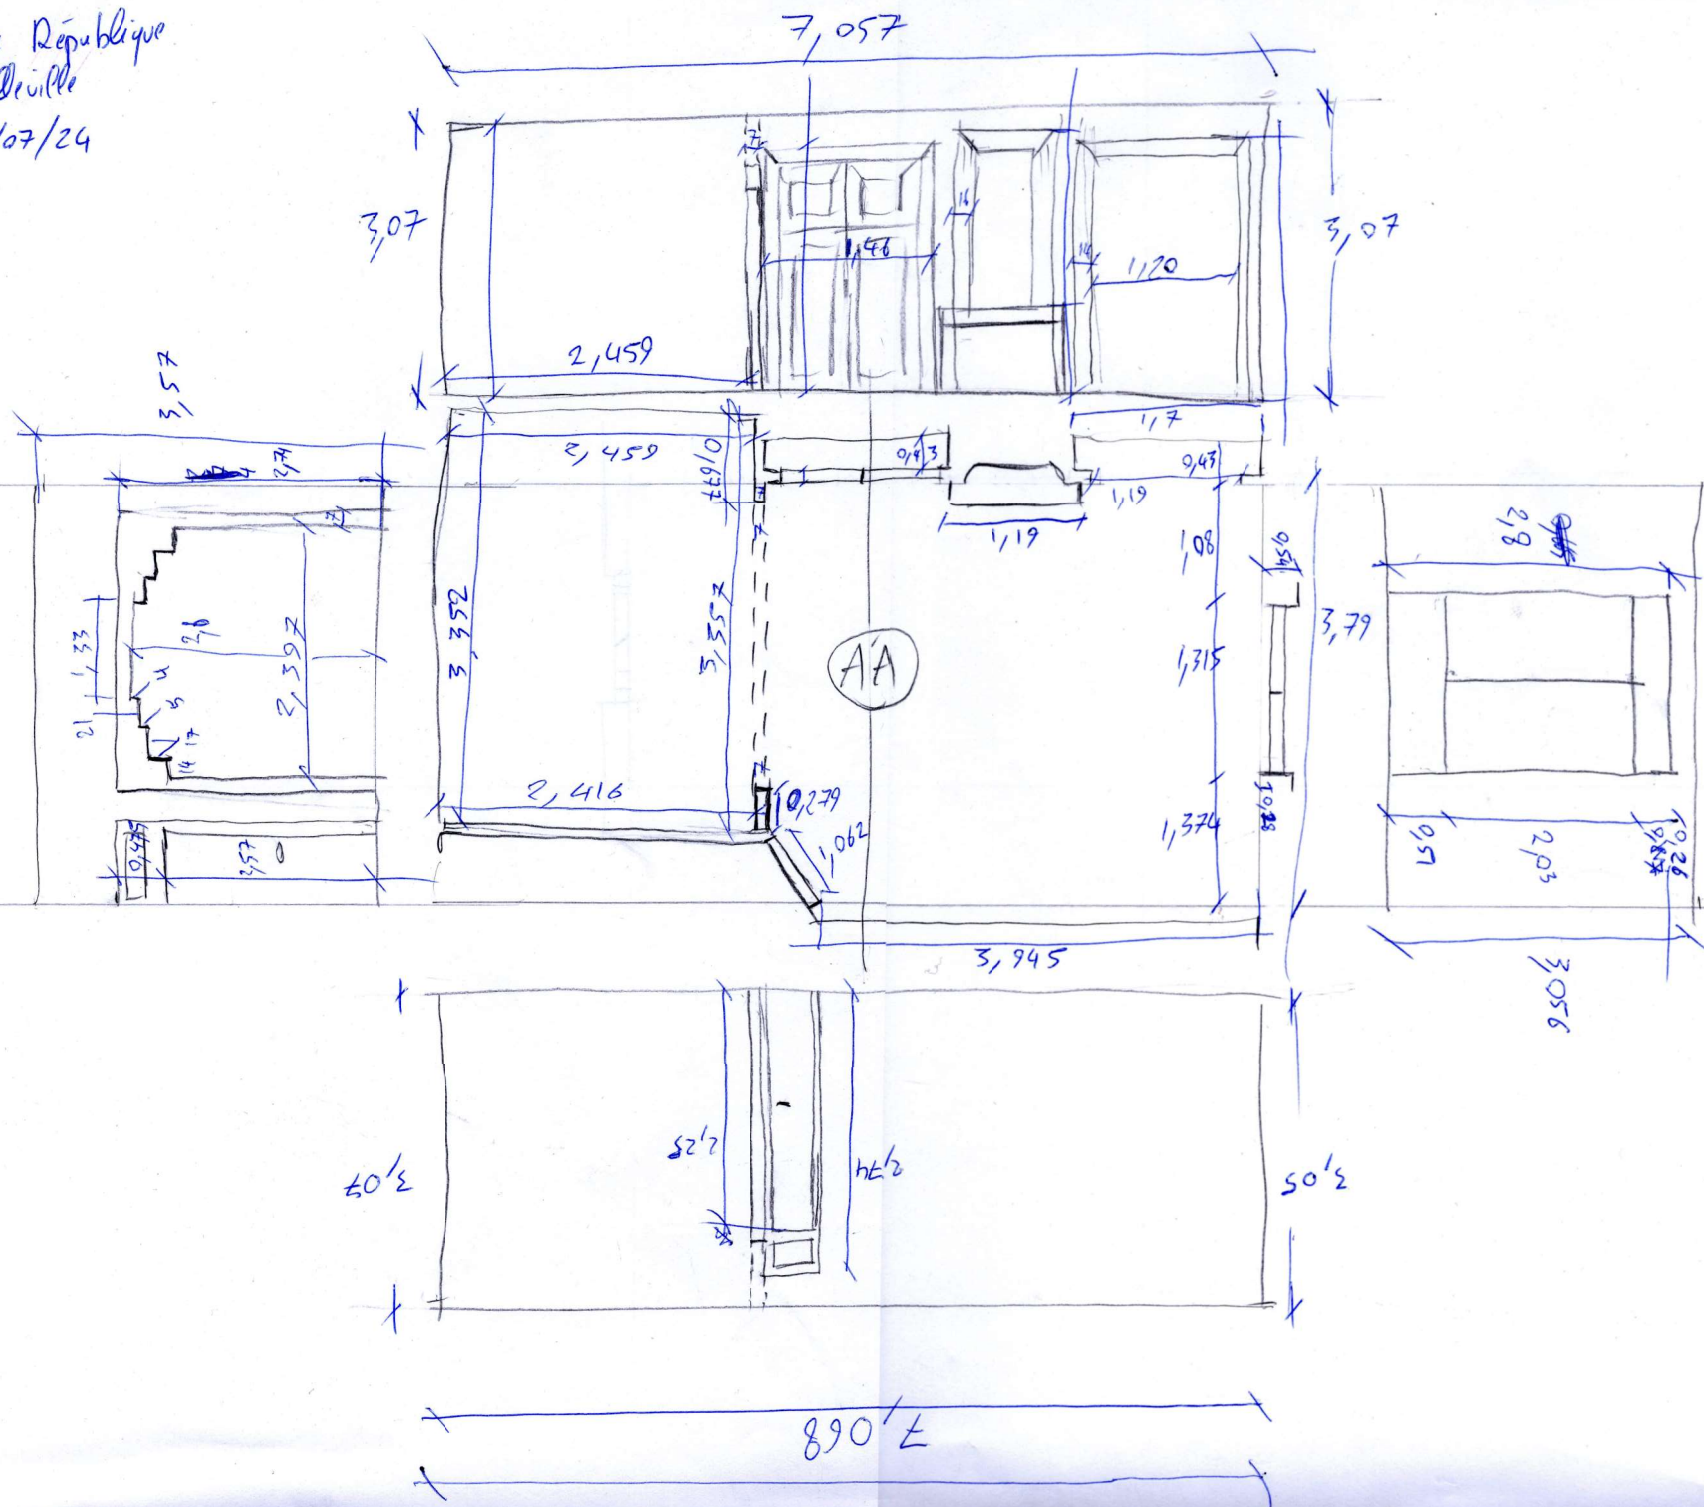

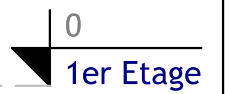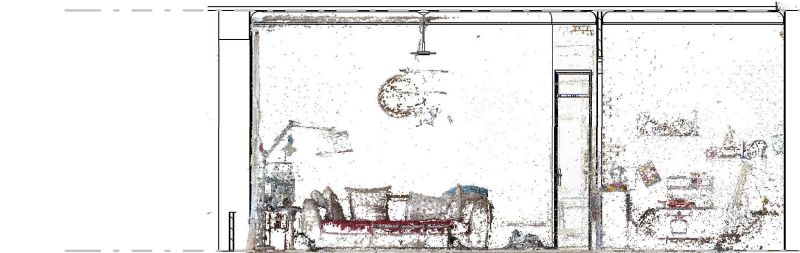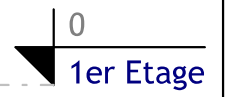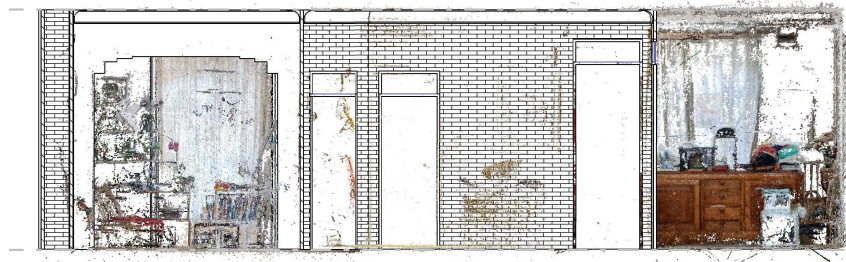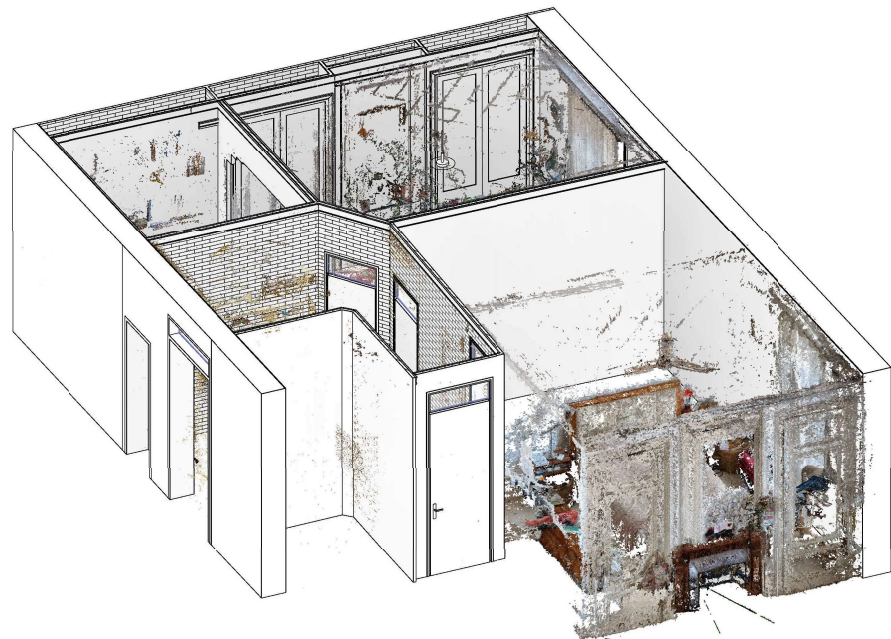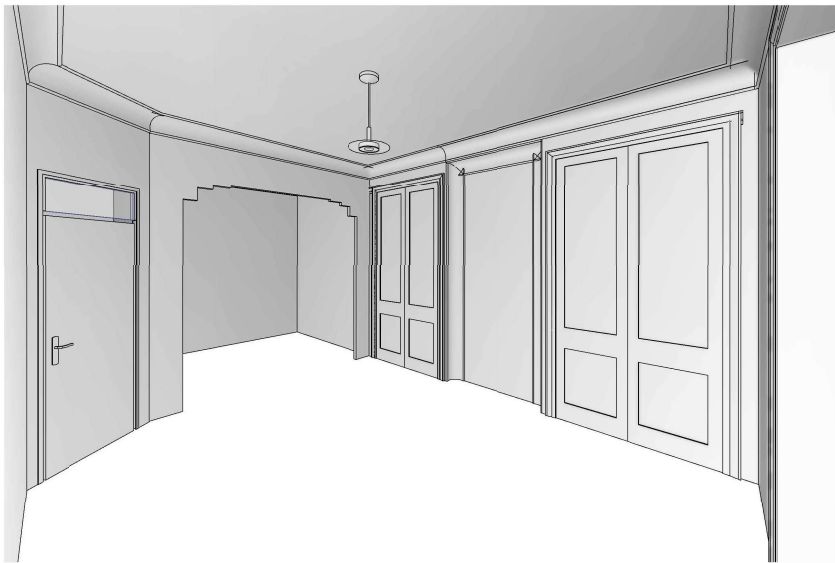

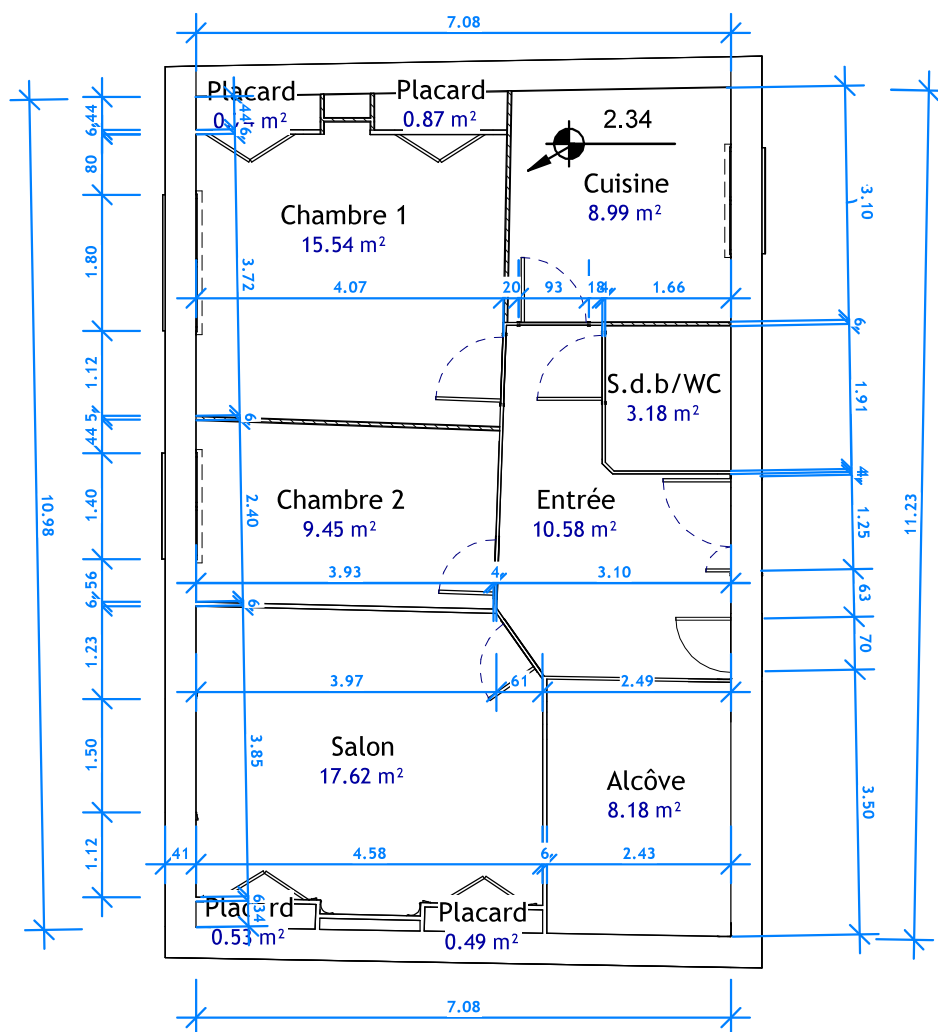

Ce document est un support pédagogique, en aucun cas il ne doit être exploité comme document réel.

Colmar	DULLIER G	07/24	1 : 100
	Remise au propre		
	1er étage		A01

Propriété dite : Zakariae

Située : Pre M'diq Fnideq M'té Martil Lieu dit Faddan Elward

Titre : 92 58/76

Echelle : 1/200


Plan levé en : Nov 2012

Limite de la propriété

D.I du 12-10-2012

5726

Régulation 466/76

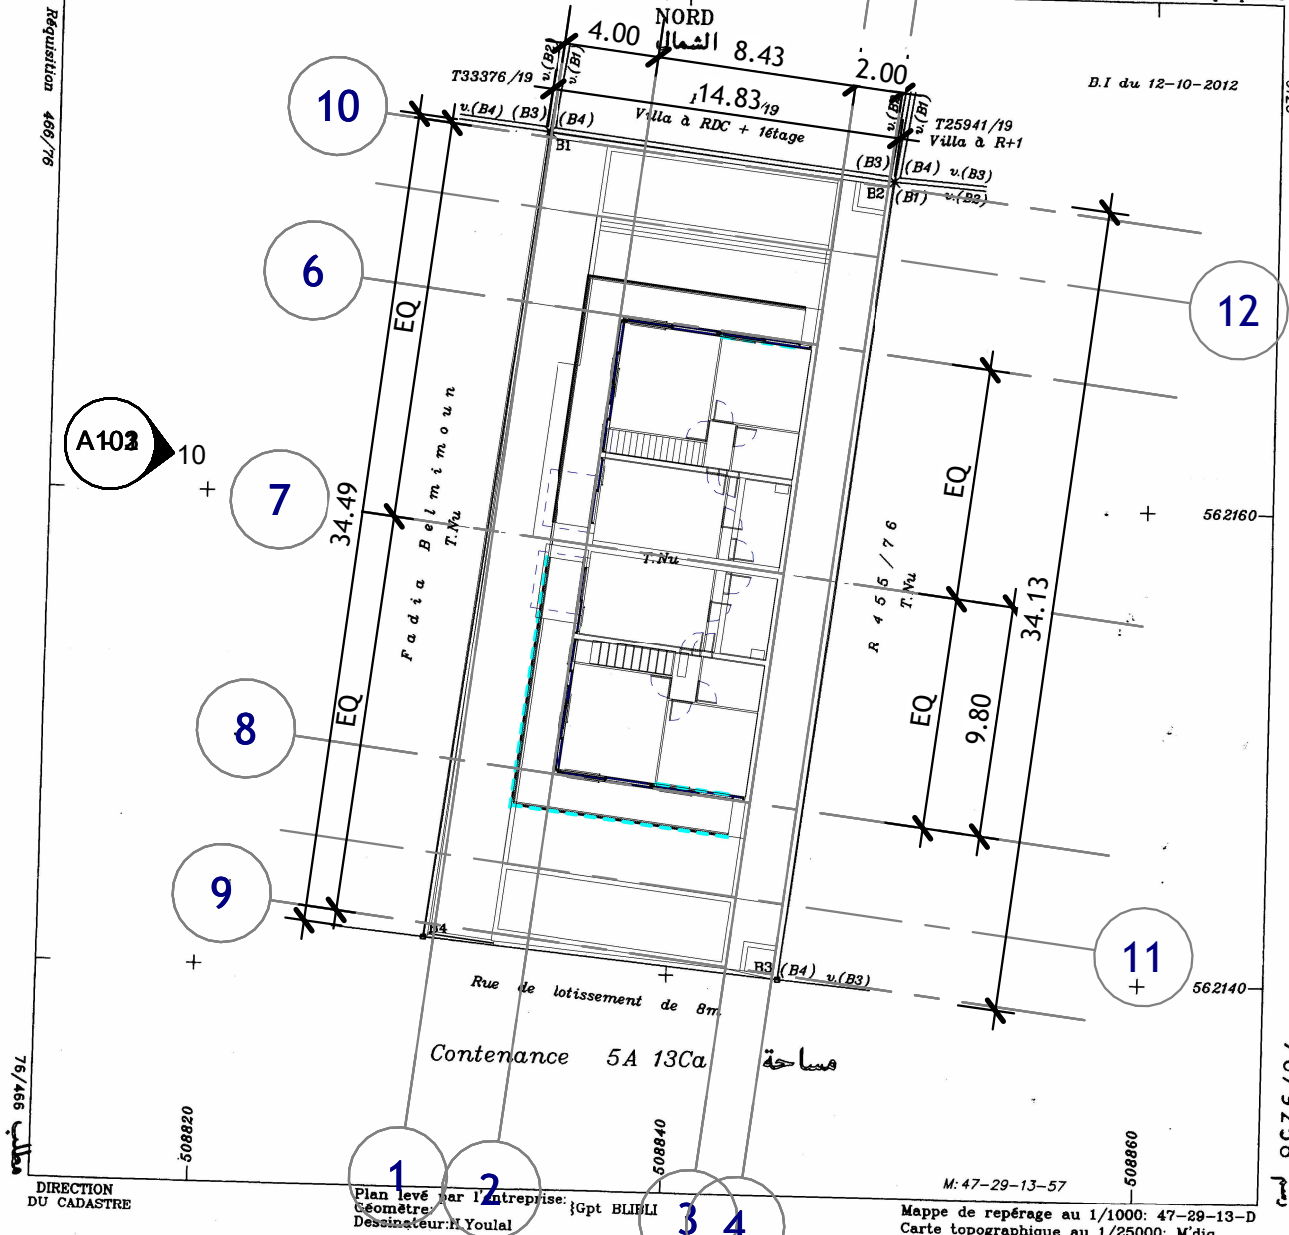

المالك المسمى زكرياء
الكاظمي
الكاظمي
8526/97
نسب

DIRECTION
DU CADASTRE



Plan levé par l'entreprise : Gpt BLIELI
Géomètre :
Dessinateur : H. Youlal




M: 47-29-13-57

Mappe de repérage au 1/1000: 47-29-13-D
Carte topographique au 1/25000: M'diq

11

A103

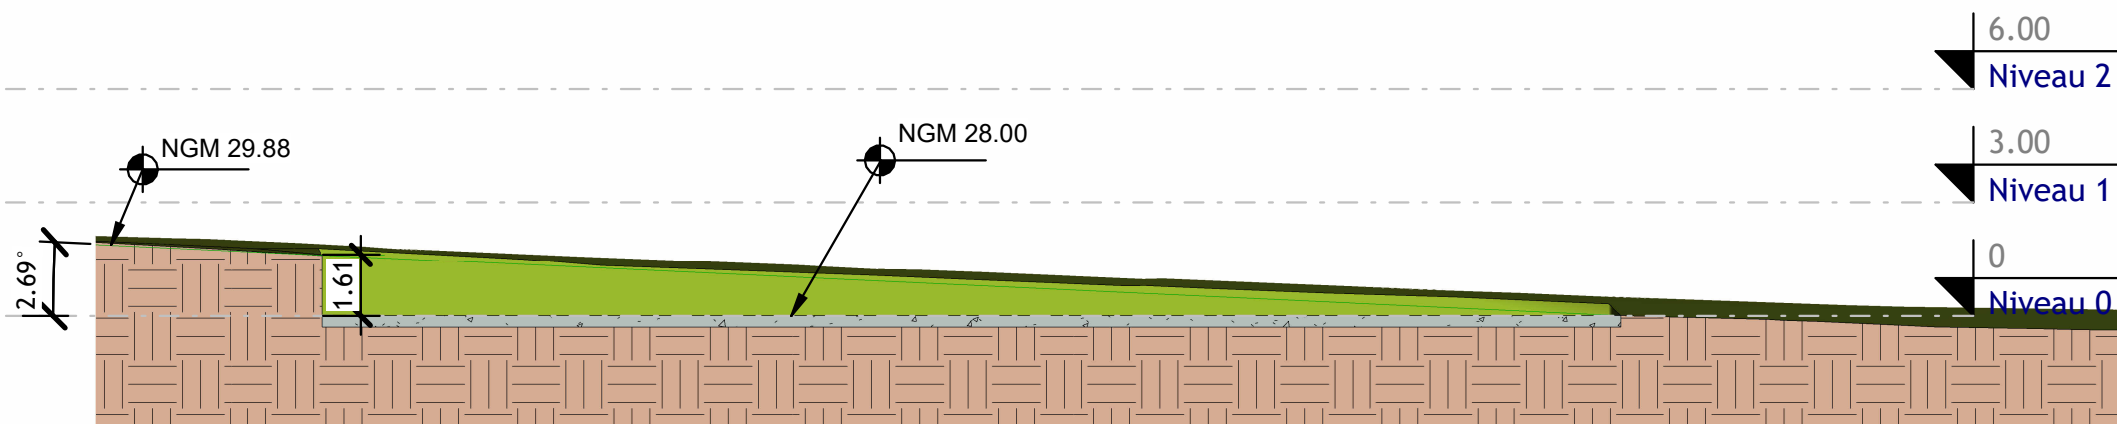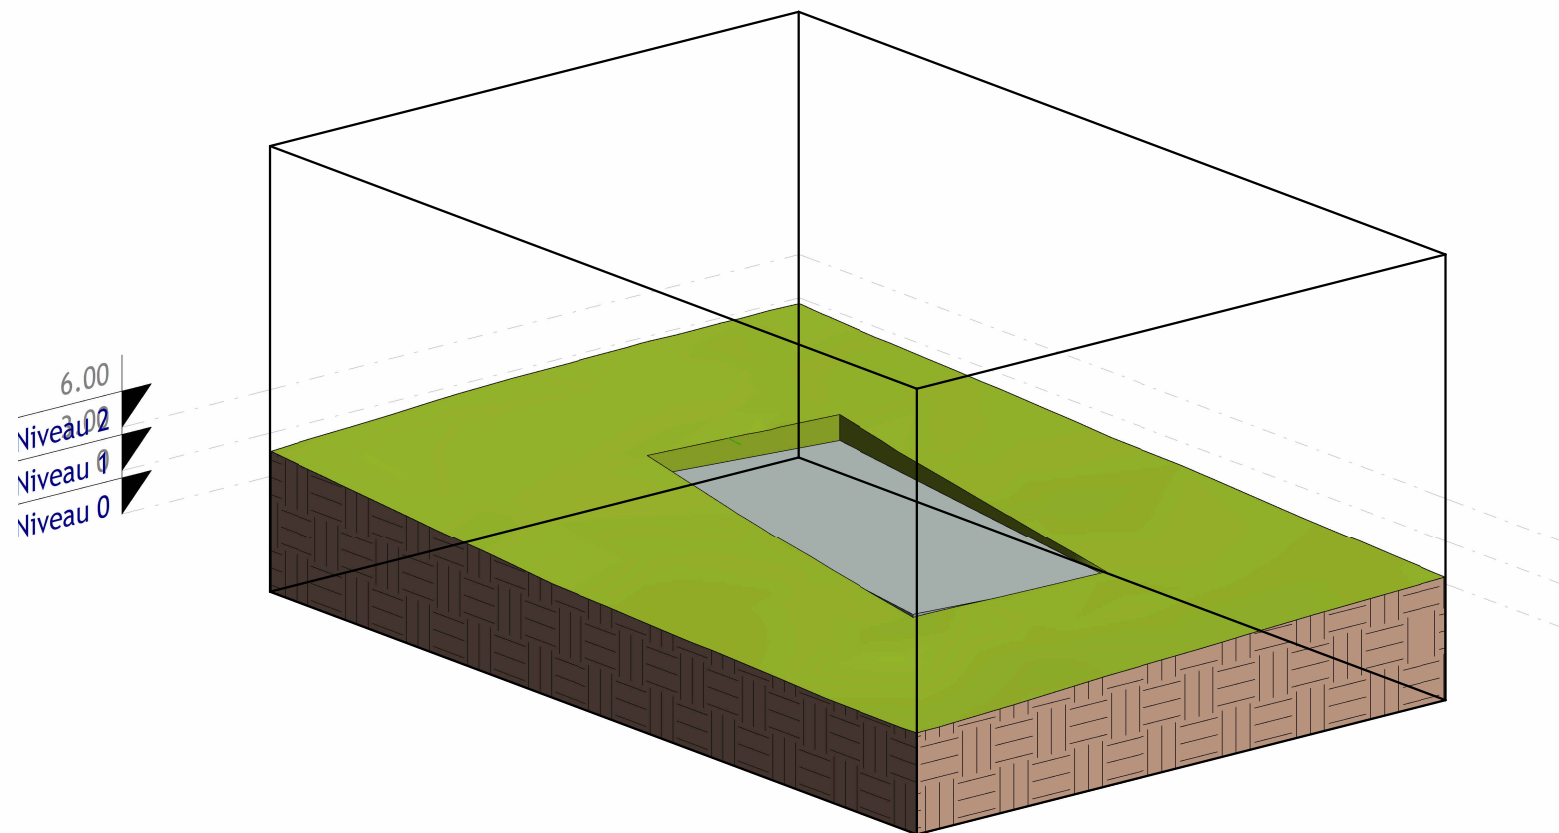

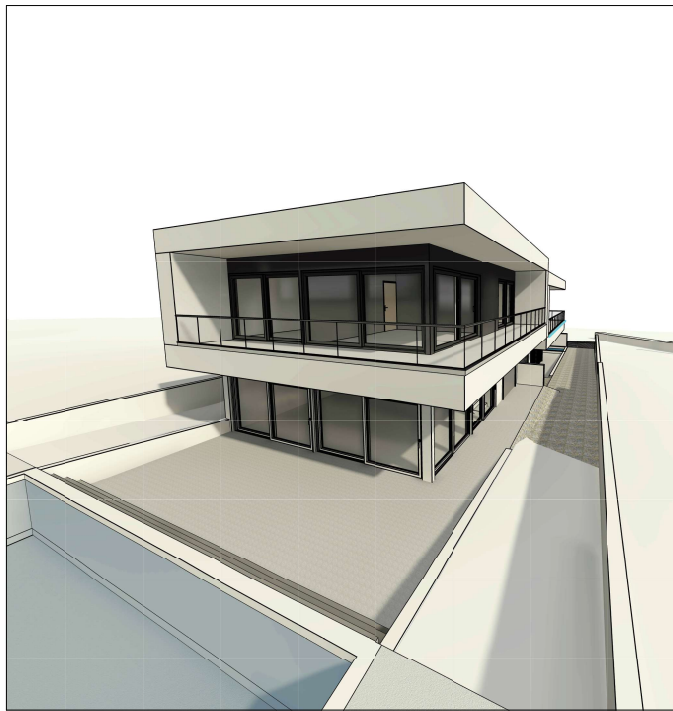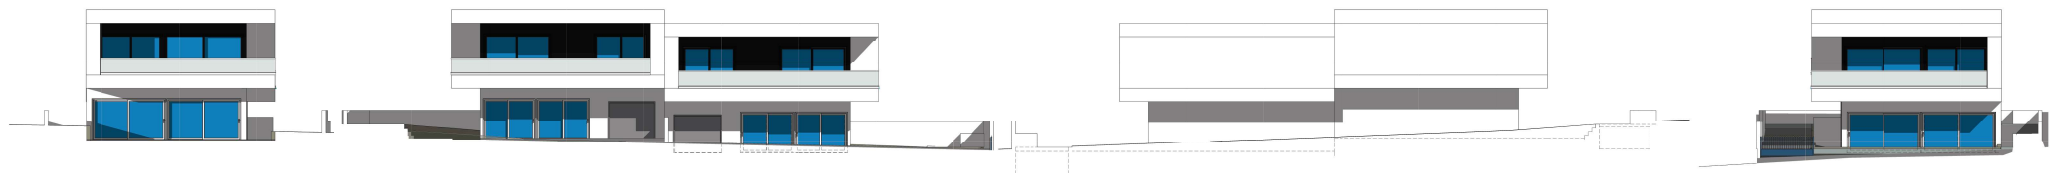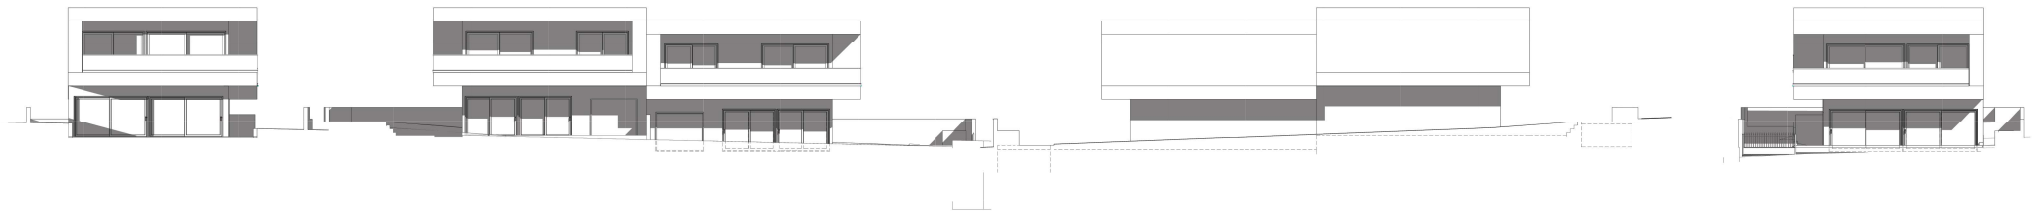


Vue 3D 1 Copie 1



Vue 3D 2 Copie 1



Vue 3D 3 Copie 1

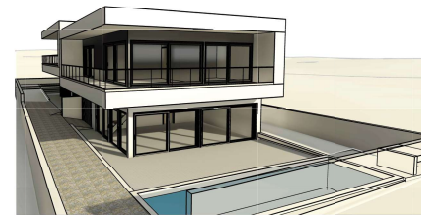

Vue 3D 4 Copie 1